


说明:

- 1、本图中外墙墙体和内墙墙体均为180厚砖墙。
- 2、除特殊注明外,本图中设备立管及留洞仅为示意,具体定位详设备专业,现场施工图时须与设备和结构图纸配合施工。设备墙体留洞,待设备安装完毕,用与墙体同级别耐火材料填充缝隙。除特殊注明外,所有洞口(除门窗外)高度均为贴结构梁底
- 3、本图中所有卫生间、有洗衣机位的阳台均向地漏找坡。
- 4、门廊及其它屋面雨水外排水口做法参12J5-1第E2页之5、第E3页之D。
- 5、本图中所有电气点位均为示意图,具体电气点位定位布置详见电施图纸。
- 6、室外台阶栏杆做法参12J9-1第108页之1,竖向杆件净距 ≤ 110 ,栏杆扶手顶部允许水平荷载标准值 1.0KN/m ,踏步防滑处理详装修图纸。
- 7、厨房污水管穿楼板做法详建施-22。WL包管材料详二次装修设计。
- 8、入口平台坡度为1%,坡向室外;卫生间坡度为1.0%,坡向地漏;边户防火挑板排水坡度为5%,中间户及连接处户型防火挑板排水坡度为1%。
- 9、各设备专业所需预留洞口均以各专业图纸为准。
- 10、精装修项目中厨房烟道、卫生间排气道外侧应用砌体、一体板、挂网抹灰等形式封闭后再铺贴瓷砖或石材,禁止直接贴在烟道或排气道上。

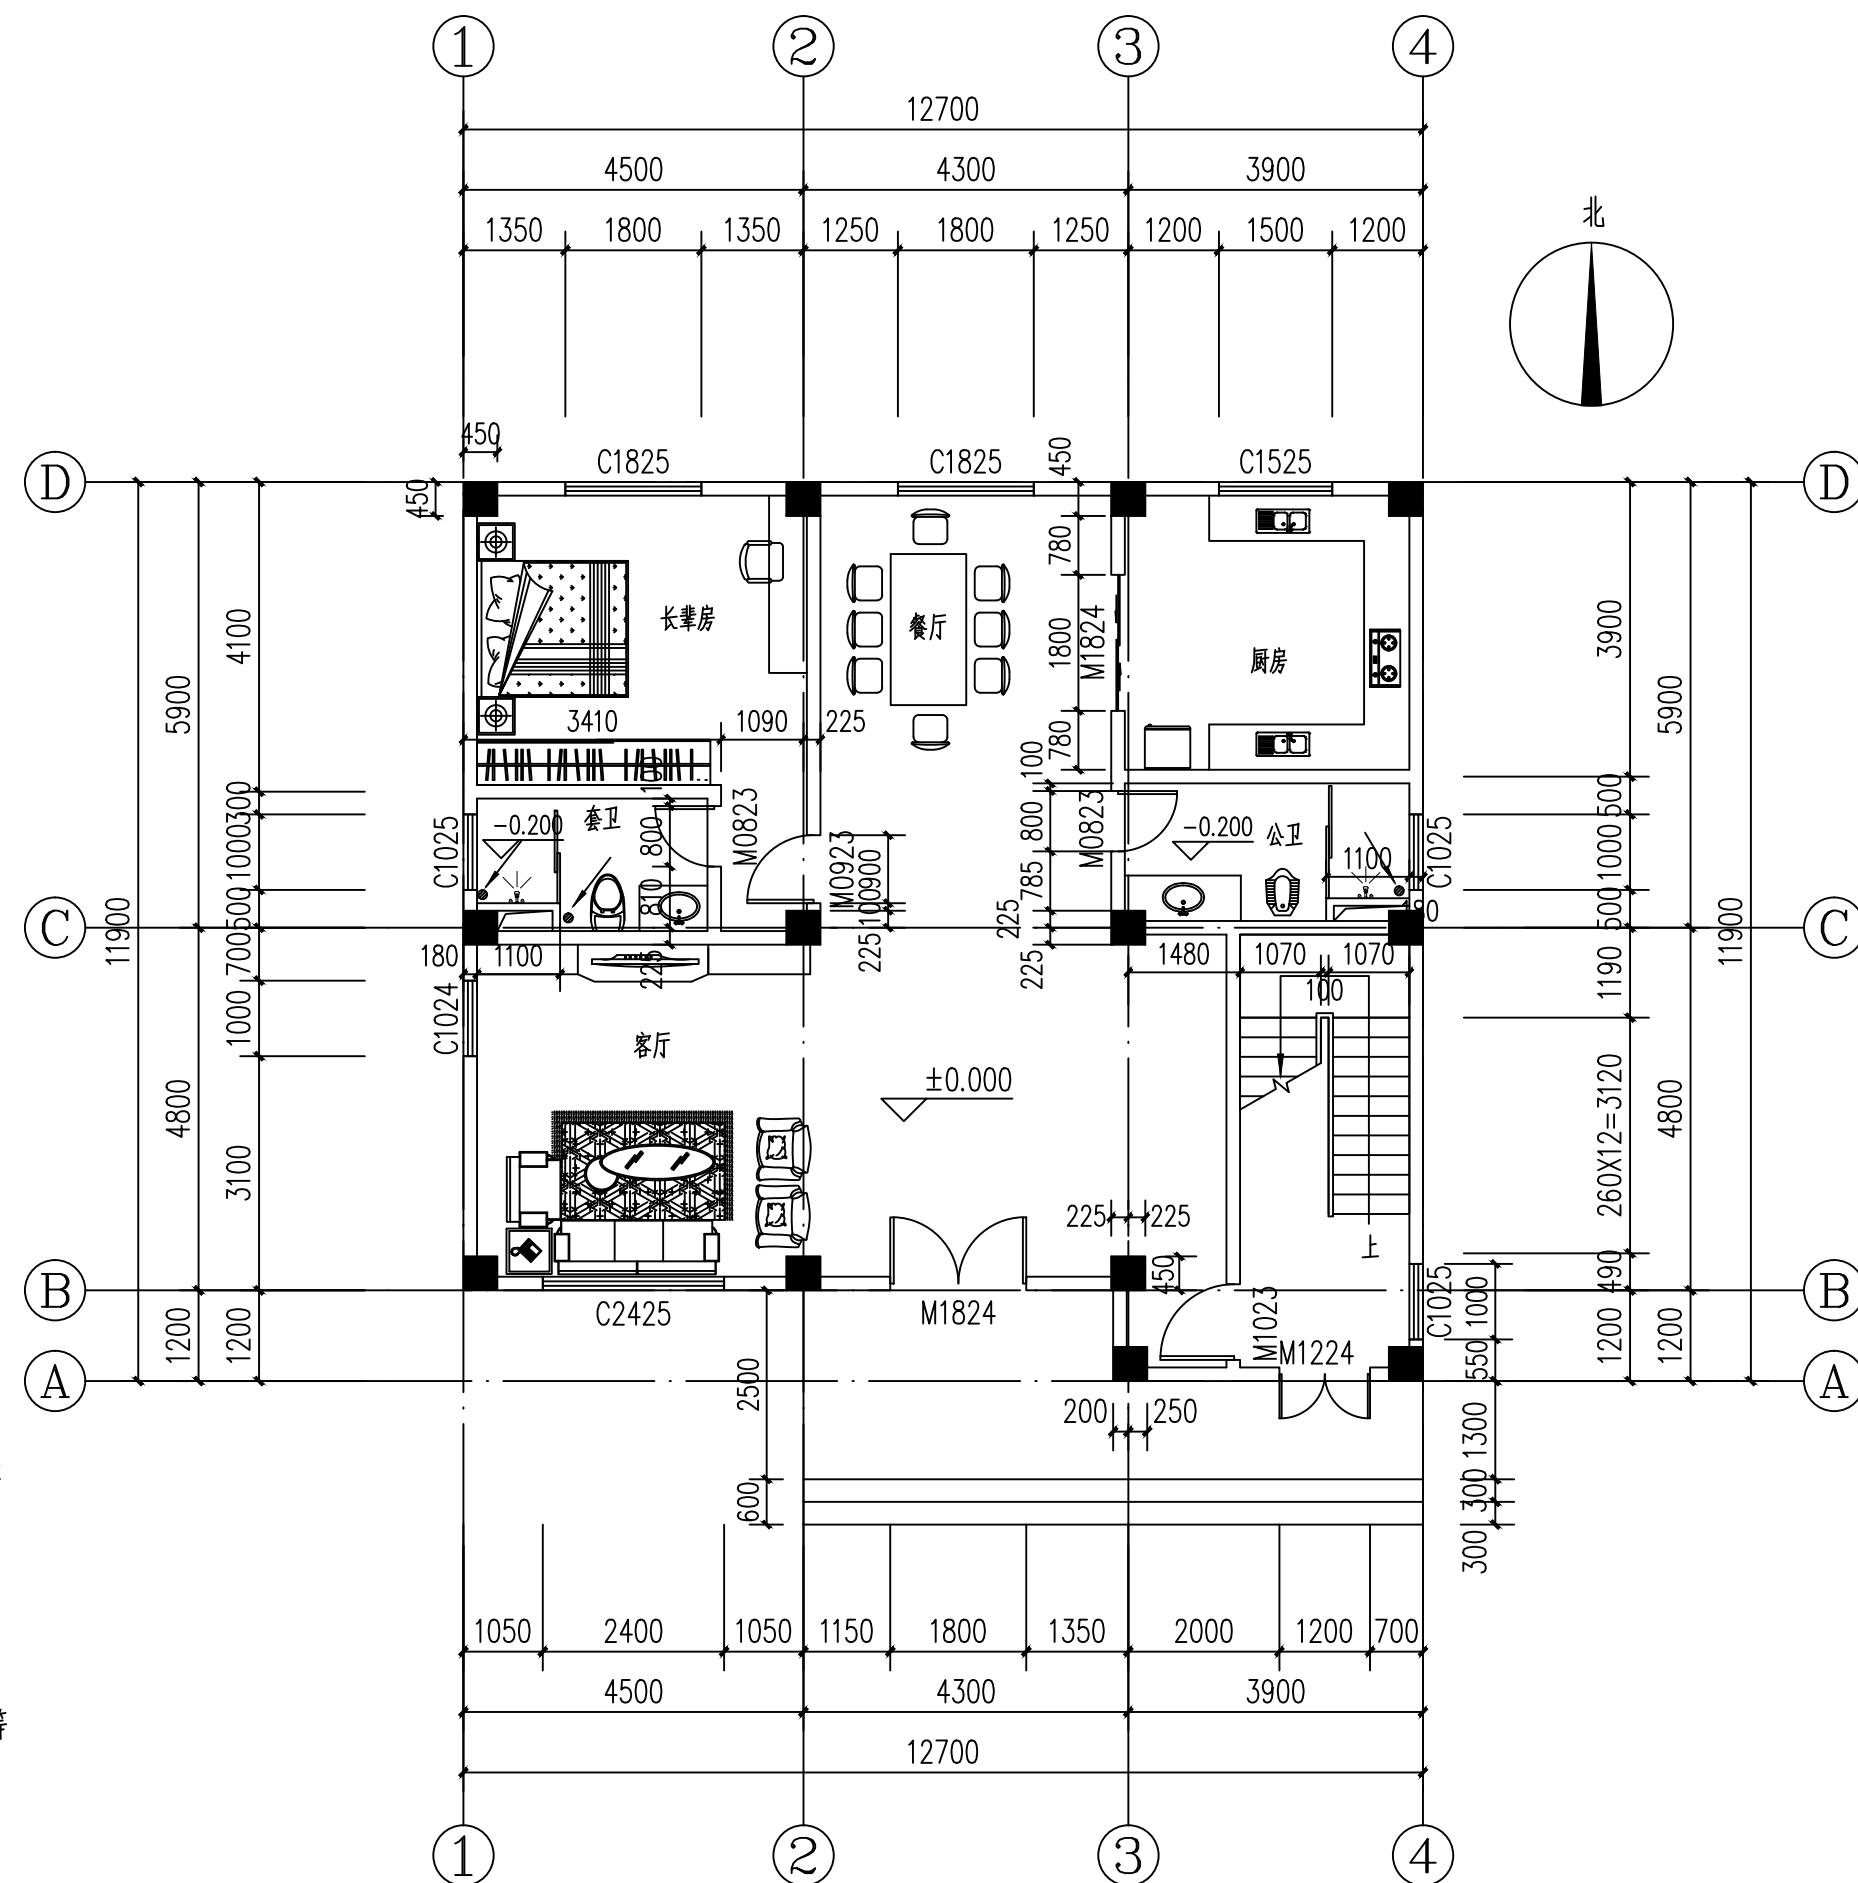


一层平面图 1:100

图名	三层顶板配筋图
图号	结施-11

说明:

- 1、本图中外墙墙体和内墙墙体均为180厚砖墙。
- 2、除特殊注明外，本图中设备立管及留洞仅为示意，具体定位详设备专业，现场施工图时须与设备和结构图纸配合施工。设备墙体留洞，待设备安装完毕，用与墙体同级别耐火材料填充缝隙。除特殊注明外，所有洞口(除门窗外)高度均为贴结构梁底。
- 3、本图中所有卫生间、有洗衣机位的阳台均向地漏找坡。
- 4、门廊及其它屋面雨水外排水口做法参12J5-1第E2页之5、第E3页之D。
- 5、本图中所有电气点位均为示意图，具体电气点位定位布置详见电施图纸。
- 6、室外台阶栏杆做法参12J9-1第108页之1，竖向杆件净距 ≤ 110 ，栏杆扶手顶部允许水平荷载标准值 1.0KN/m ，踏步防滑处理详装修图纸。
- 7、厨房污水管穿楼板做法详建施-22。WL包管材料详二次装修设计。
- 8、入口平台坡度为1%，坡向室外；卫生间坡度为1.0%，坡向地漏；边户防火挑板排水坡度为5%，中间户及连接处户型防火挑板排水坡度为1%。
- 9、各设备专业所需预留洞口均以各专业图纸为准。
- 10、精装修项目中厨房烟道、卫生间排气道外侧应用砌体、一体板、挂网抹灰等形式封闭后再铺贴瓷砖或石材，禁止直接贴在烟道或排气道上。

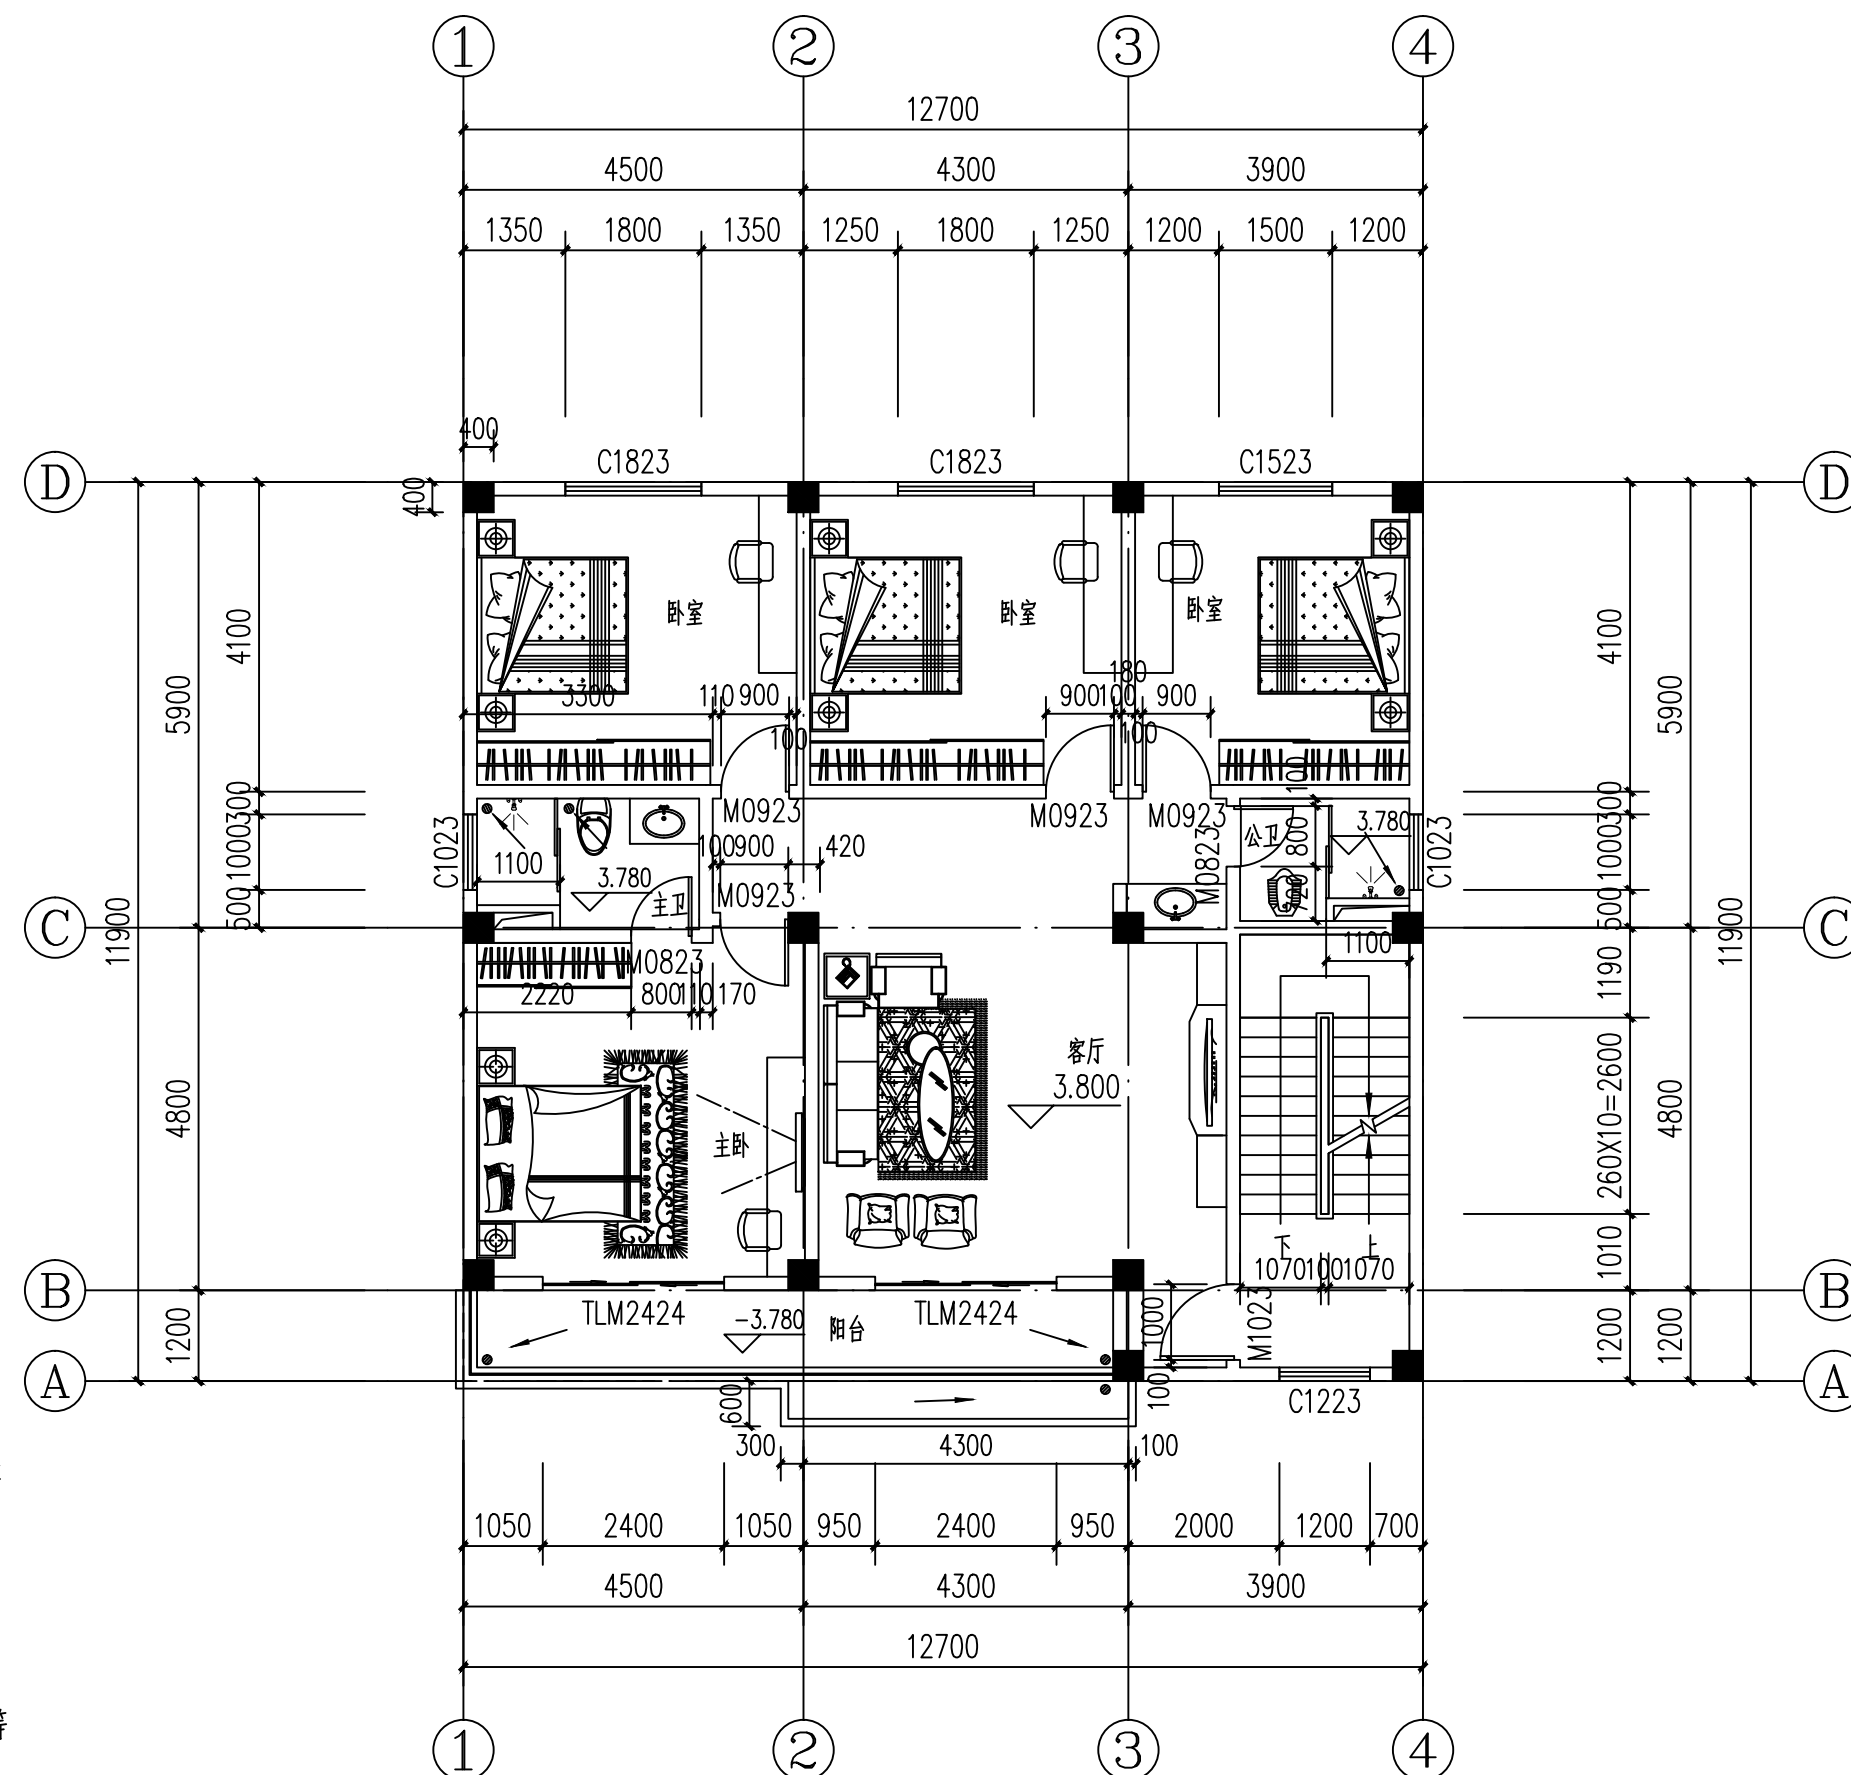


二层平面图 1:100

图名	三层顶板配筋图
图号	结施-11

说明:

- 1、本图中外墙墙体和内墙墙体均为180厚砖墙。
- 2、除特殊注明外,本图中设备立管及留洞仅为示意,具体定位详设备专业,现场施工图时须与设备和结构图纸配合施工。设备墙体留洞,待设备安装完毕,用与墙体同级别耐火材料填充缝隙。除特殊注明外,所有洞口(除门窗外)高度均为贴结构梁底。
- 3、本图中所有卫生间、有洗衣机位的阳台均向地漏找坡。
- 4、门廊及其它屋面雨水外排水口做法参12J5-1第E2页之5、第E3页之D。
- 5、本图中所有电气点位均为示意图,具体电气点位布置详见电施图纸。
- 6、室外台阶栏杆做法参12J9-1第108页之1,竖向杆件净距 ≤ 110 ,栏杆扶手顶部允许水平荷载标准值 1.0KN/m ,踏步防滑处理详装修图纸。
- 7、厨房污水管穿楼板做法详建施-22。WL包管材料详二次装修设计。
- 8、入口平台坡度为1%,坡向室外;卫生间坡度为1.0%,坡向地漏;边户防火挑板排水坡度为5%,中间户及连接处户型防火挑板排水坡度为1%。
- 9、各设备专业所需预留洞口均以各专业图纸为准。
- 10、精装修项目中厨房烟道、卫生间排气道外侧应用砌体、一体板、挂网抹灰等形式封闭后再铺贴瓷砖或石材,禁止直接贴在烟道或排气道上。

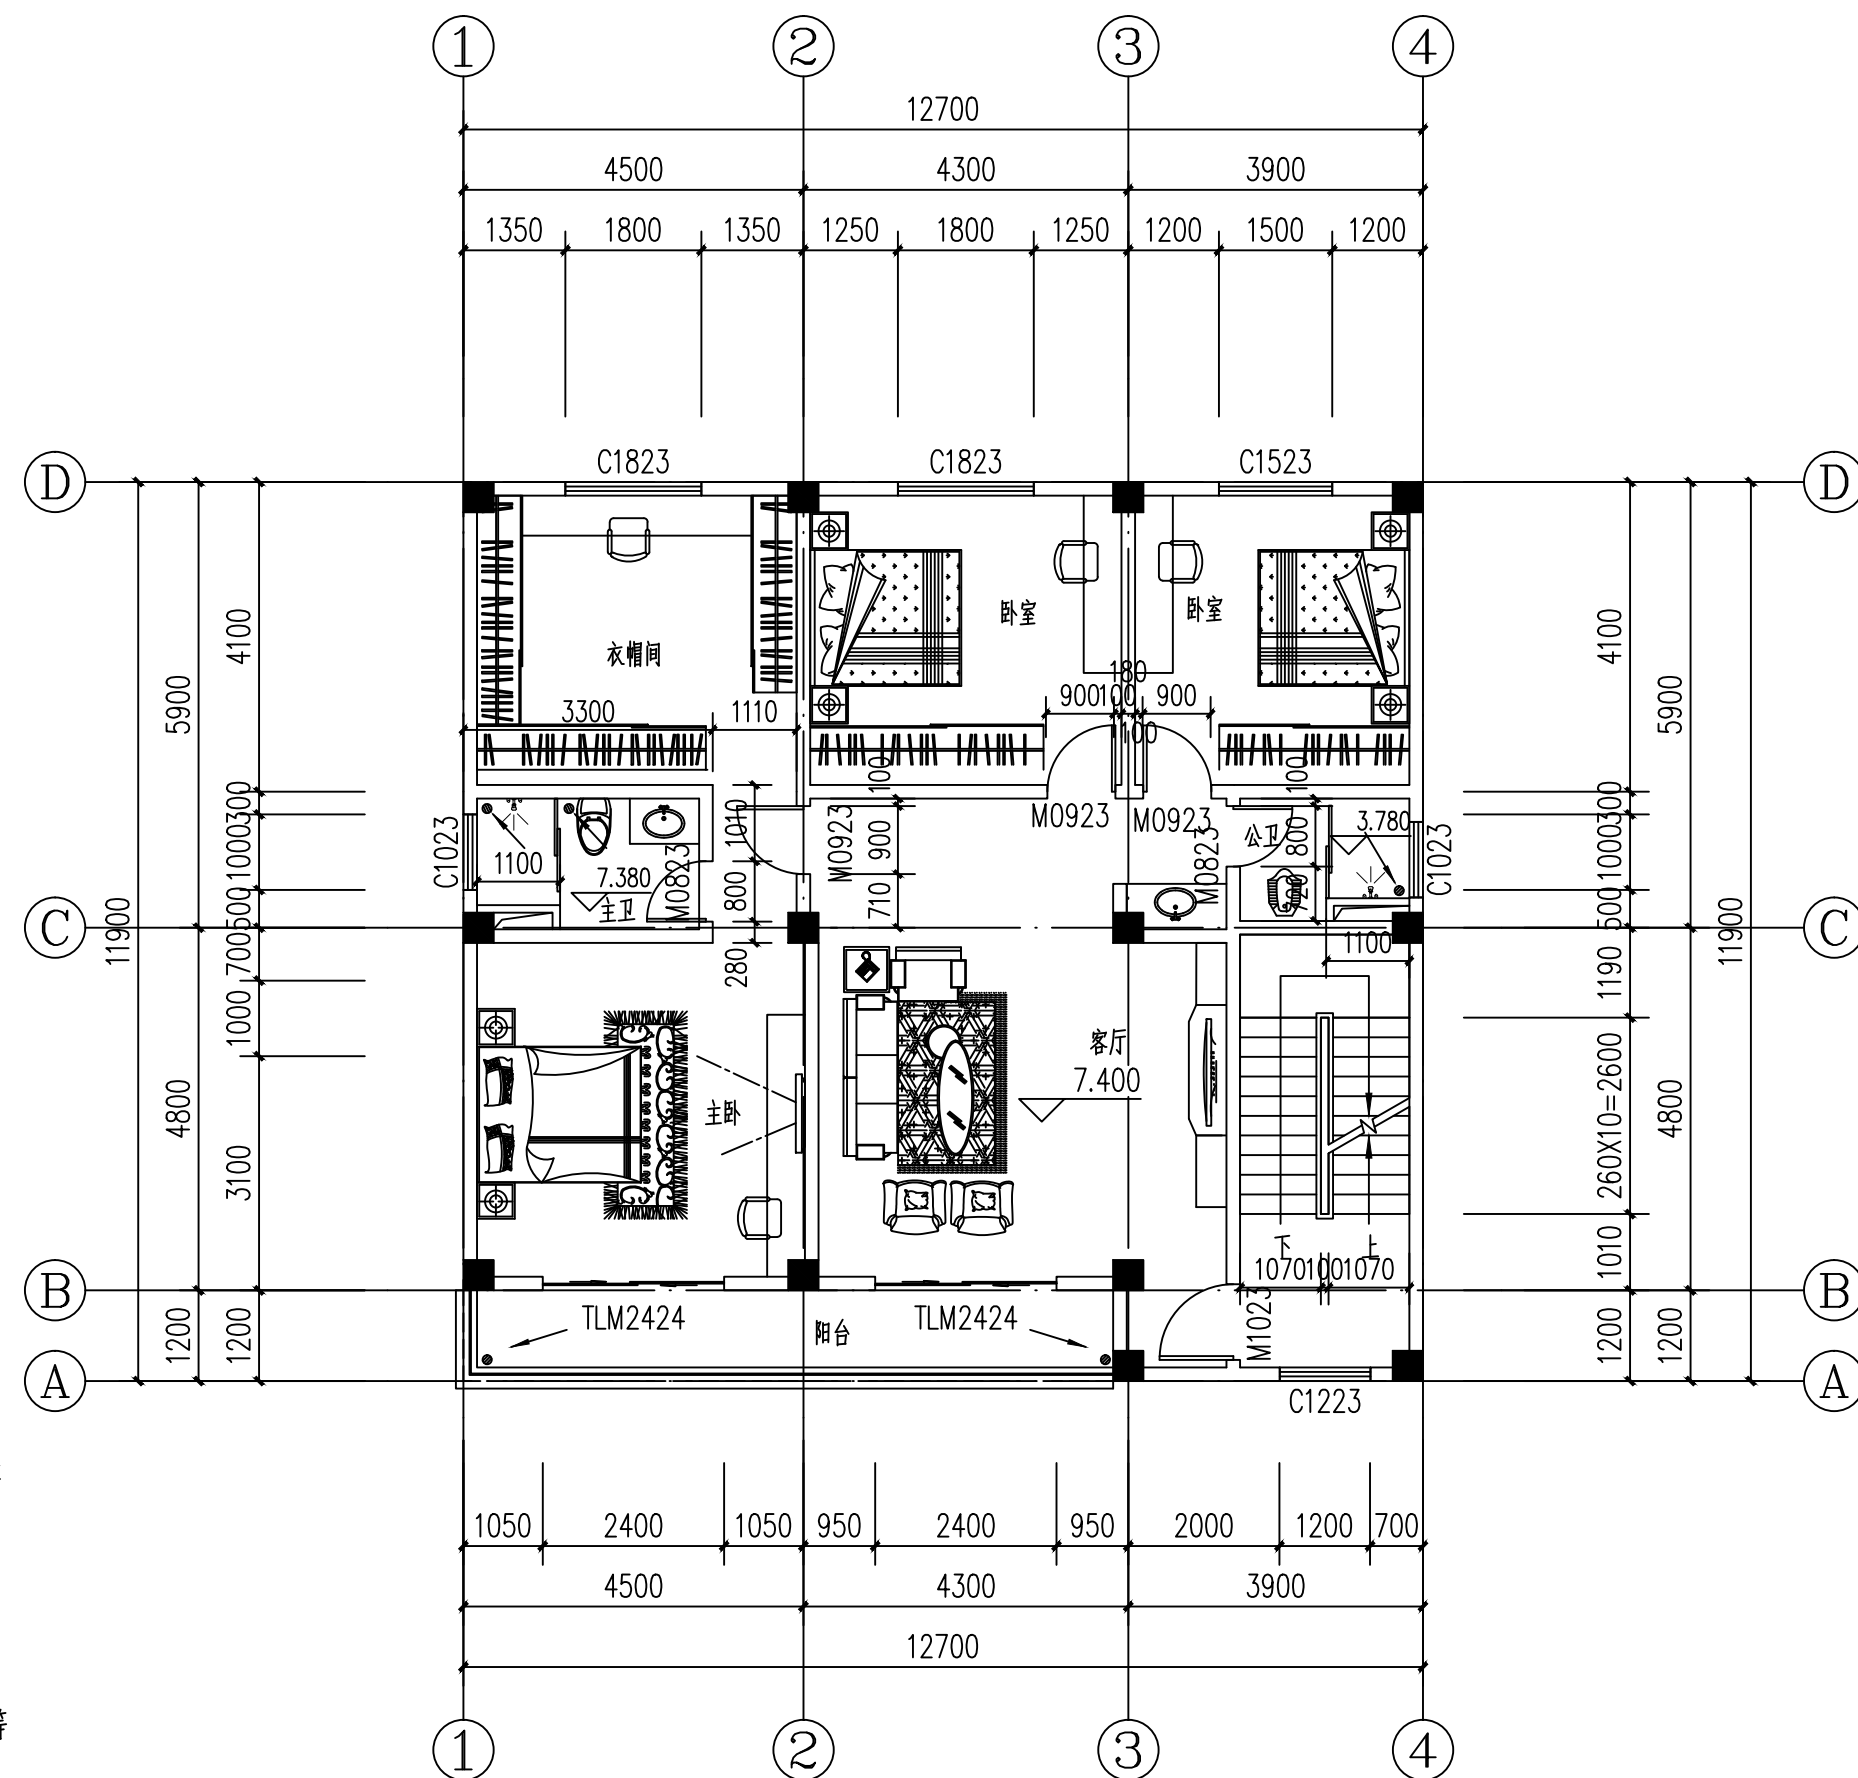


三层平面图 1:100

图名	三层顶板配筋图
图号	结施-11

说明:

- 1、本图中外墙墙体和内墙墙体均为180厚砖墙。
- 2、除特殊注明外,本图中设备立管及留洞仅为示意,具体定位详设备专业,现场施工图时须与设备和结构图纸配合施工。设备墙体留洞,待设备安装完毕,用与墙体同级别耐火材料填充缝隙。除特殊注明外,所有洞口(除门窗外)高度均为贴结构梁底
- 3、本图中所有卫生间、有洗衣机位的阳台均向地漏找坡。
- 4、门廊及其它屋面雨水外排水口做法参12J5-1第E2页之5、第E3页之D。
- 5、本图中所有电气点位均为示意图,具体电气点位定位布置详见电施图纸。
- 6、室外台阶栏杆做法参12J9-1第108页之1,竖向杆件净距 ≤ 110 ,栏杆扶手顶部允许水平荷载标准值 1.0KN/m ,踏步防滑处理详装修图纸。
- 7、厨房污水管穿楼板做法详建施-22。WL包管材料详二次装修设计。
- 8、入口平台坡度为1%,坡向室外;卫生间坡度为1.0%,坡向地漏;边户防火挑板排水坡度为5%,中间户及连接处户型防火挑板排水坡度为1%。
- 9、各设备专业所需预留洞口均以各专业图纸为准。
- 10、精装修项目中厨房烟道、卫生间排气道外侧应用砌体、一体板、挂网抹灰等形式封闭后再铺贴瓷砖或石材,禁止直接贴在烟道或排气道上。

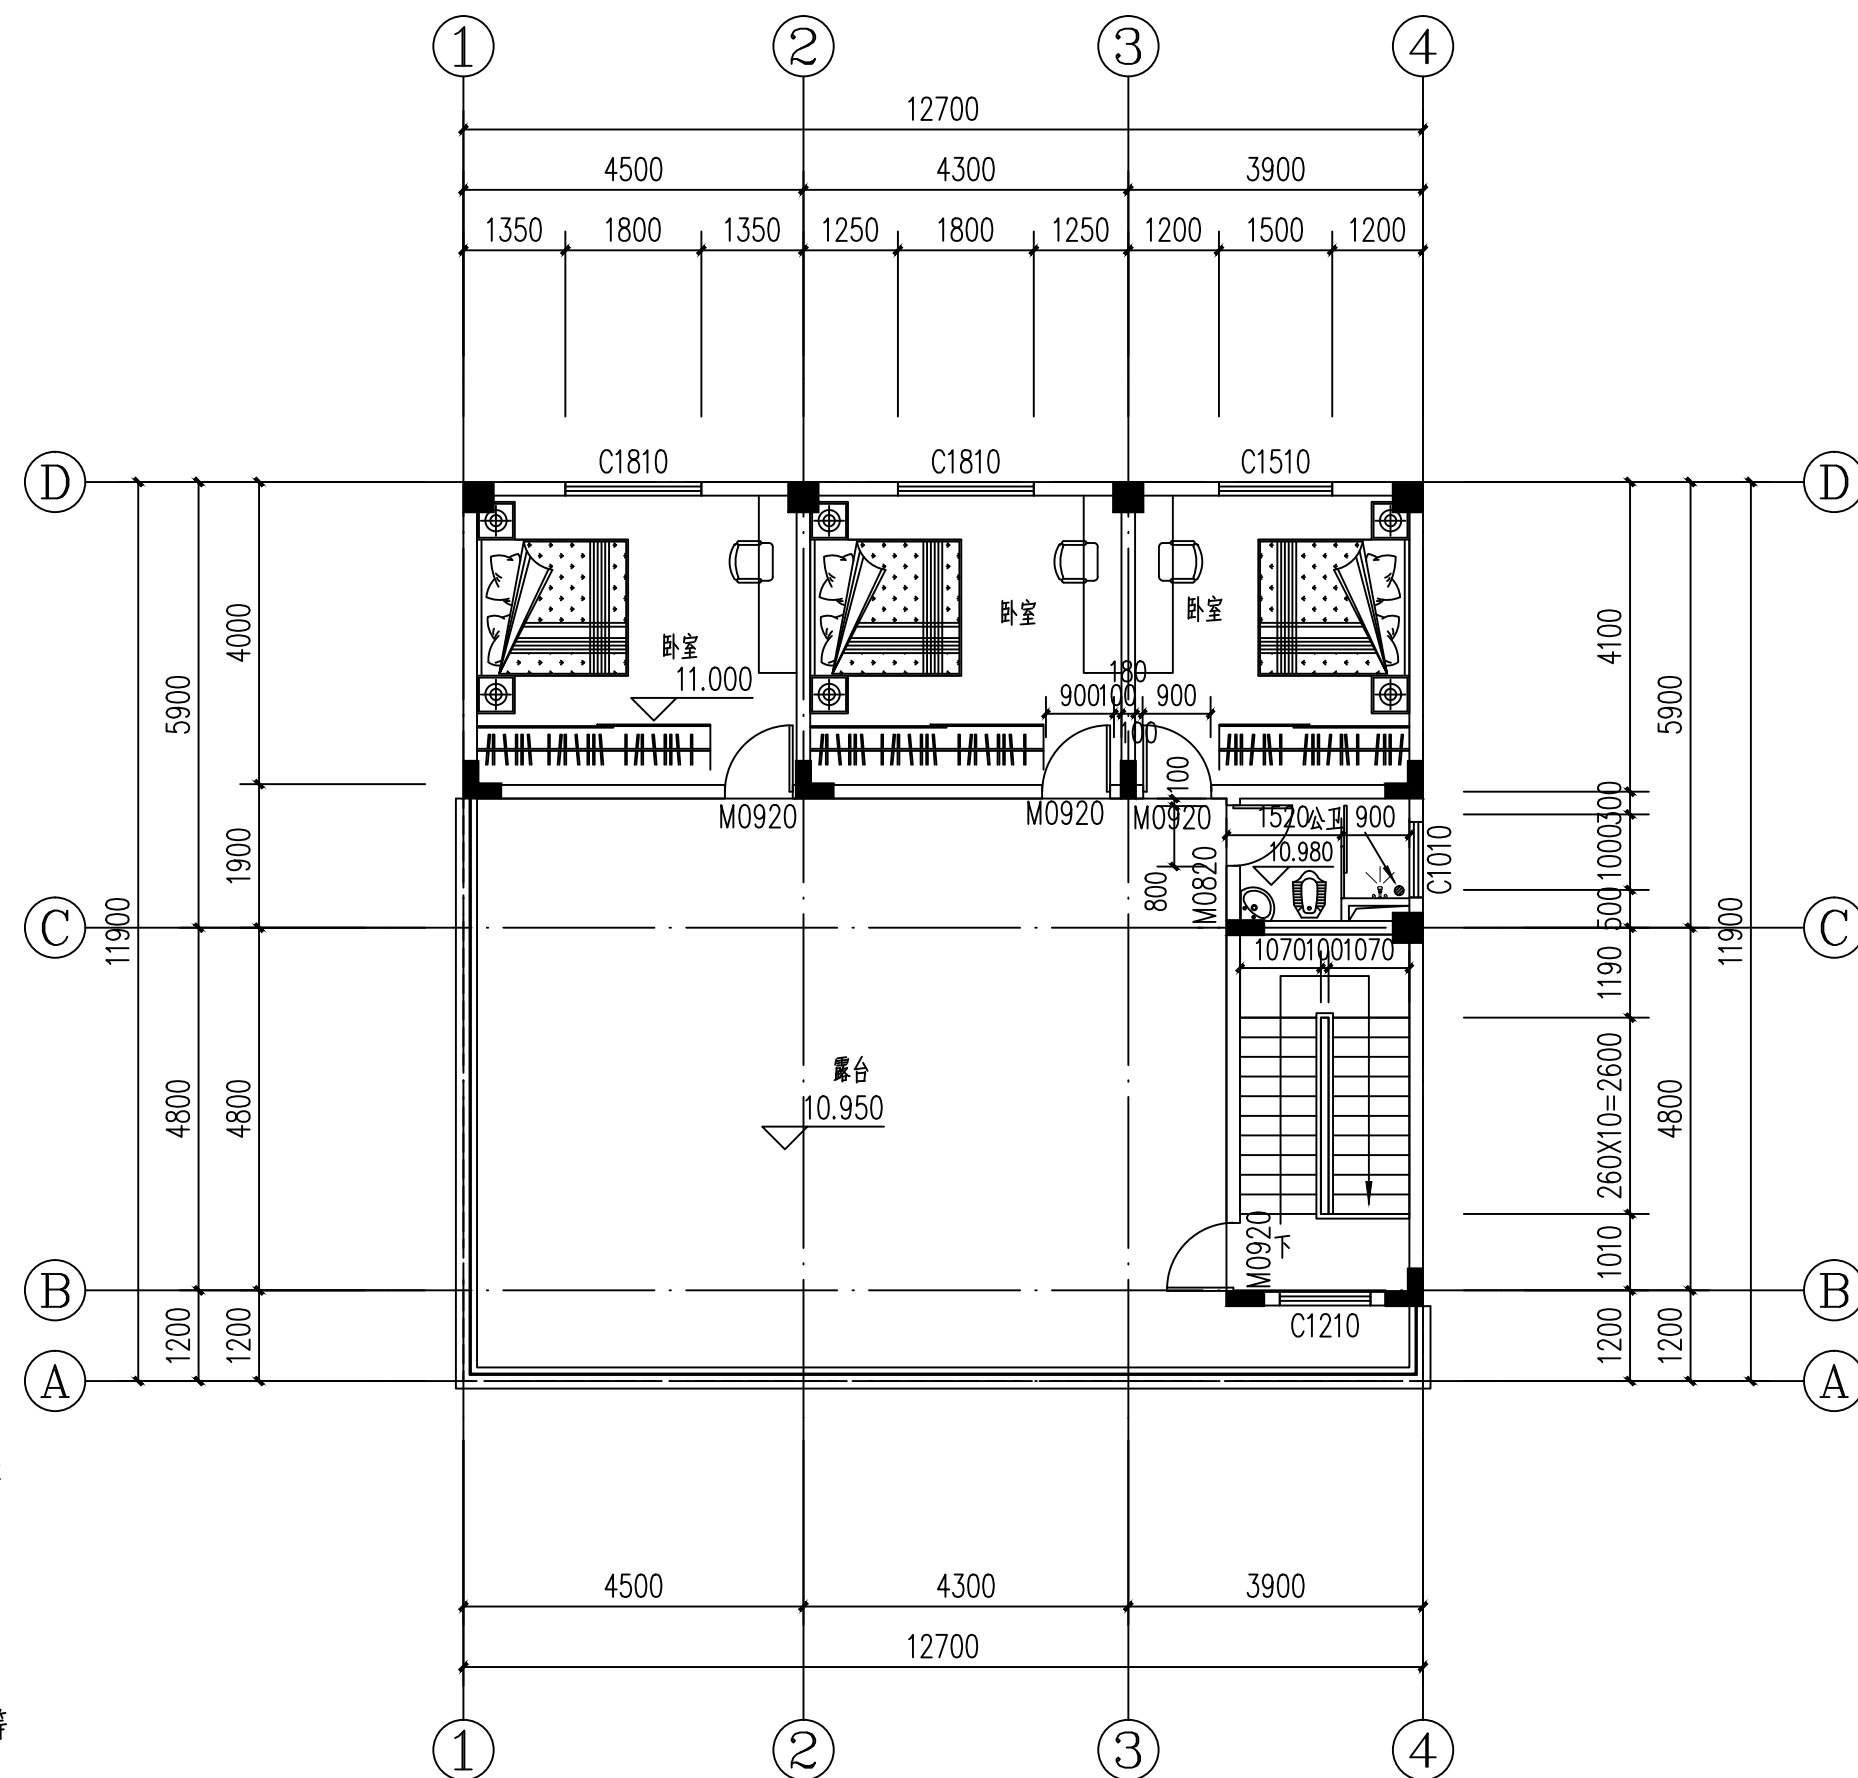


四层平面图 1:100

图名	三层顶板配筋图
图号	结施-11

说明:

- 1、本图中外墙墙体和内墙墙体均为180厚砖墙。
- 2、除特殊注明外,本图中设备立管及留洞仅为示意,具体定位详设备专业,现场施工图时须与设备和结构图纸配合施工。设备墙体留洞,待设备安装完毕,用与墙体同级别耐火材料填充缝隙。除特殊注明外,所有洞口(除门窗外)高度均为贴结构梁底
- 3、本图中所有卫生间、有洗衣机位的阳台均向地漏找坡。
- 4、门廊及其它屋面雨水外排水口做法参12J5-1第E2页之5、第E3页之D.
- 5、本图中所有电气点位均为示意图,具体电气点位定位布置详见电施图纸。
- 6、室外台阶栏杆做法参12J9-1第108页之1,竖向杆件净距 ≤ 110 ,栏杆扶手顶部允许水平荷载标准值 1.0KN/m ,踏步防滑处理详装修图纸。
- 7、厨房污水管穿楼板做法详建施-22。WL包管材料详二次装修设计。
- 8、入口平台坡度为1%,坡向室外;卫生间坡度为1.0%,坡向地漏;边户防火挑板排水坡度为5%,中间户及连接处户型防火挑板排水坡度为1%。
- 9、各设备专业所需预留洞口均以各专业图纸为准。
- 10、精装修项目中厨房烟道、卫生间排气道外侧应用砌体、一体板、挂网抹灰等形式封闭后再铺贴瓷砖或石材,禁止直接贴在烟道或排气道上。

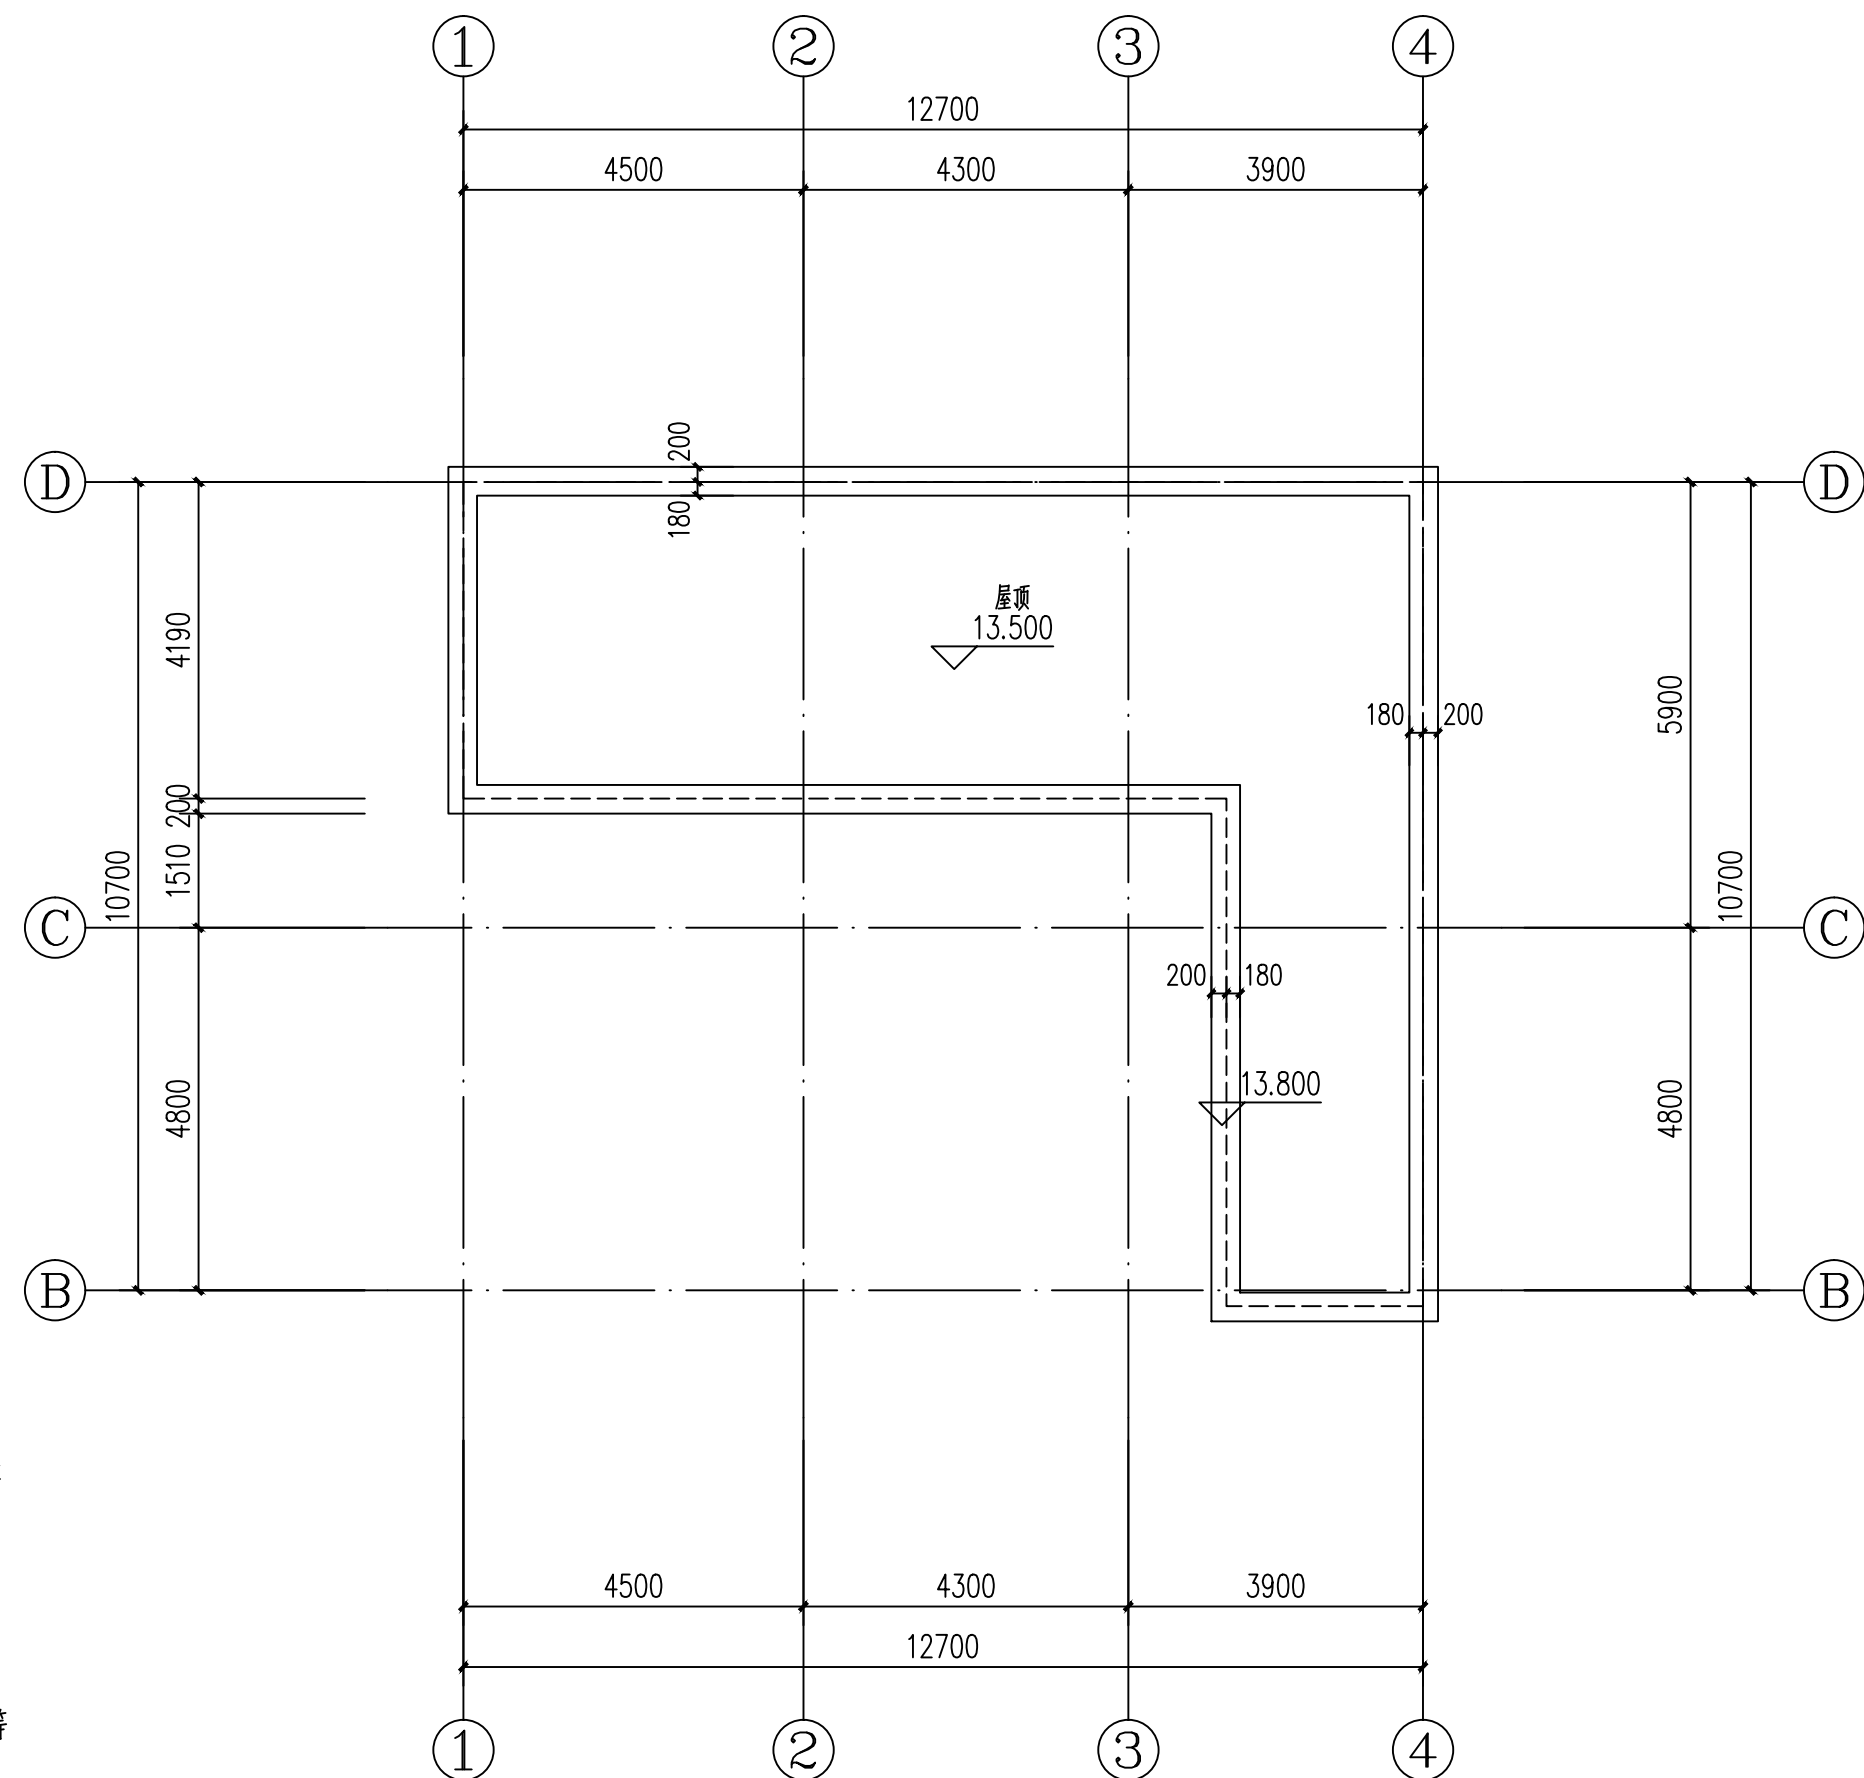

屋顶平面图 1:100

图 名	三层顶板配筋图
图 号	结施-11